


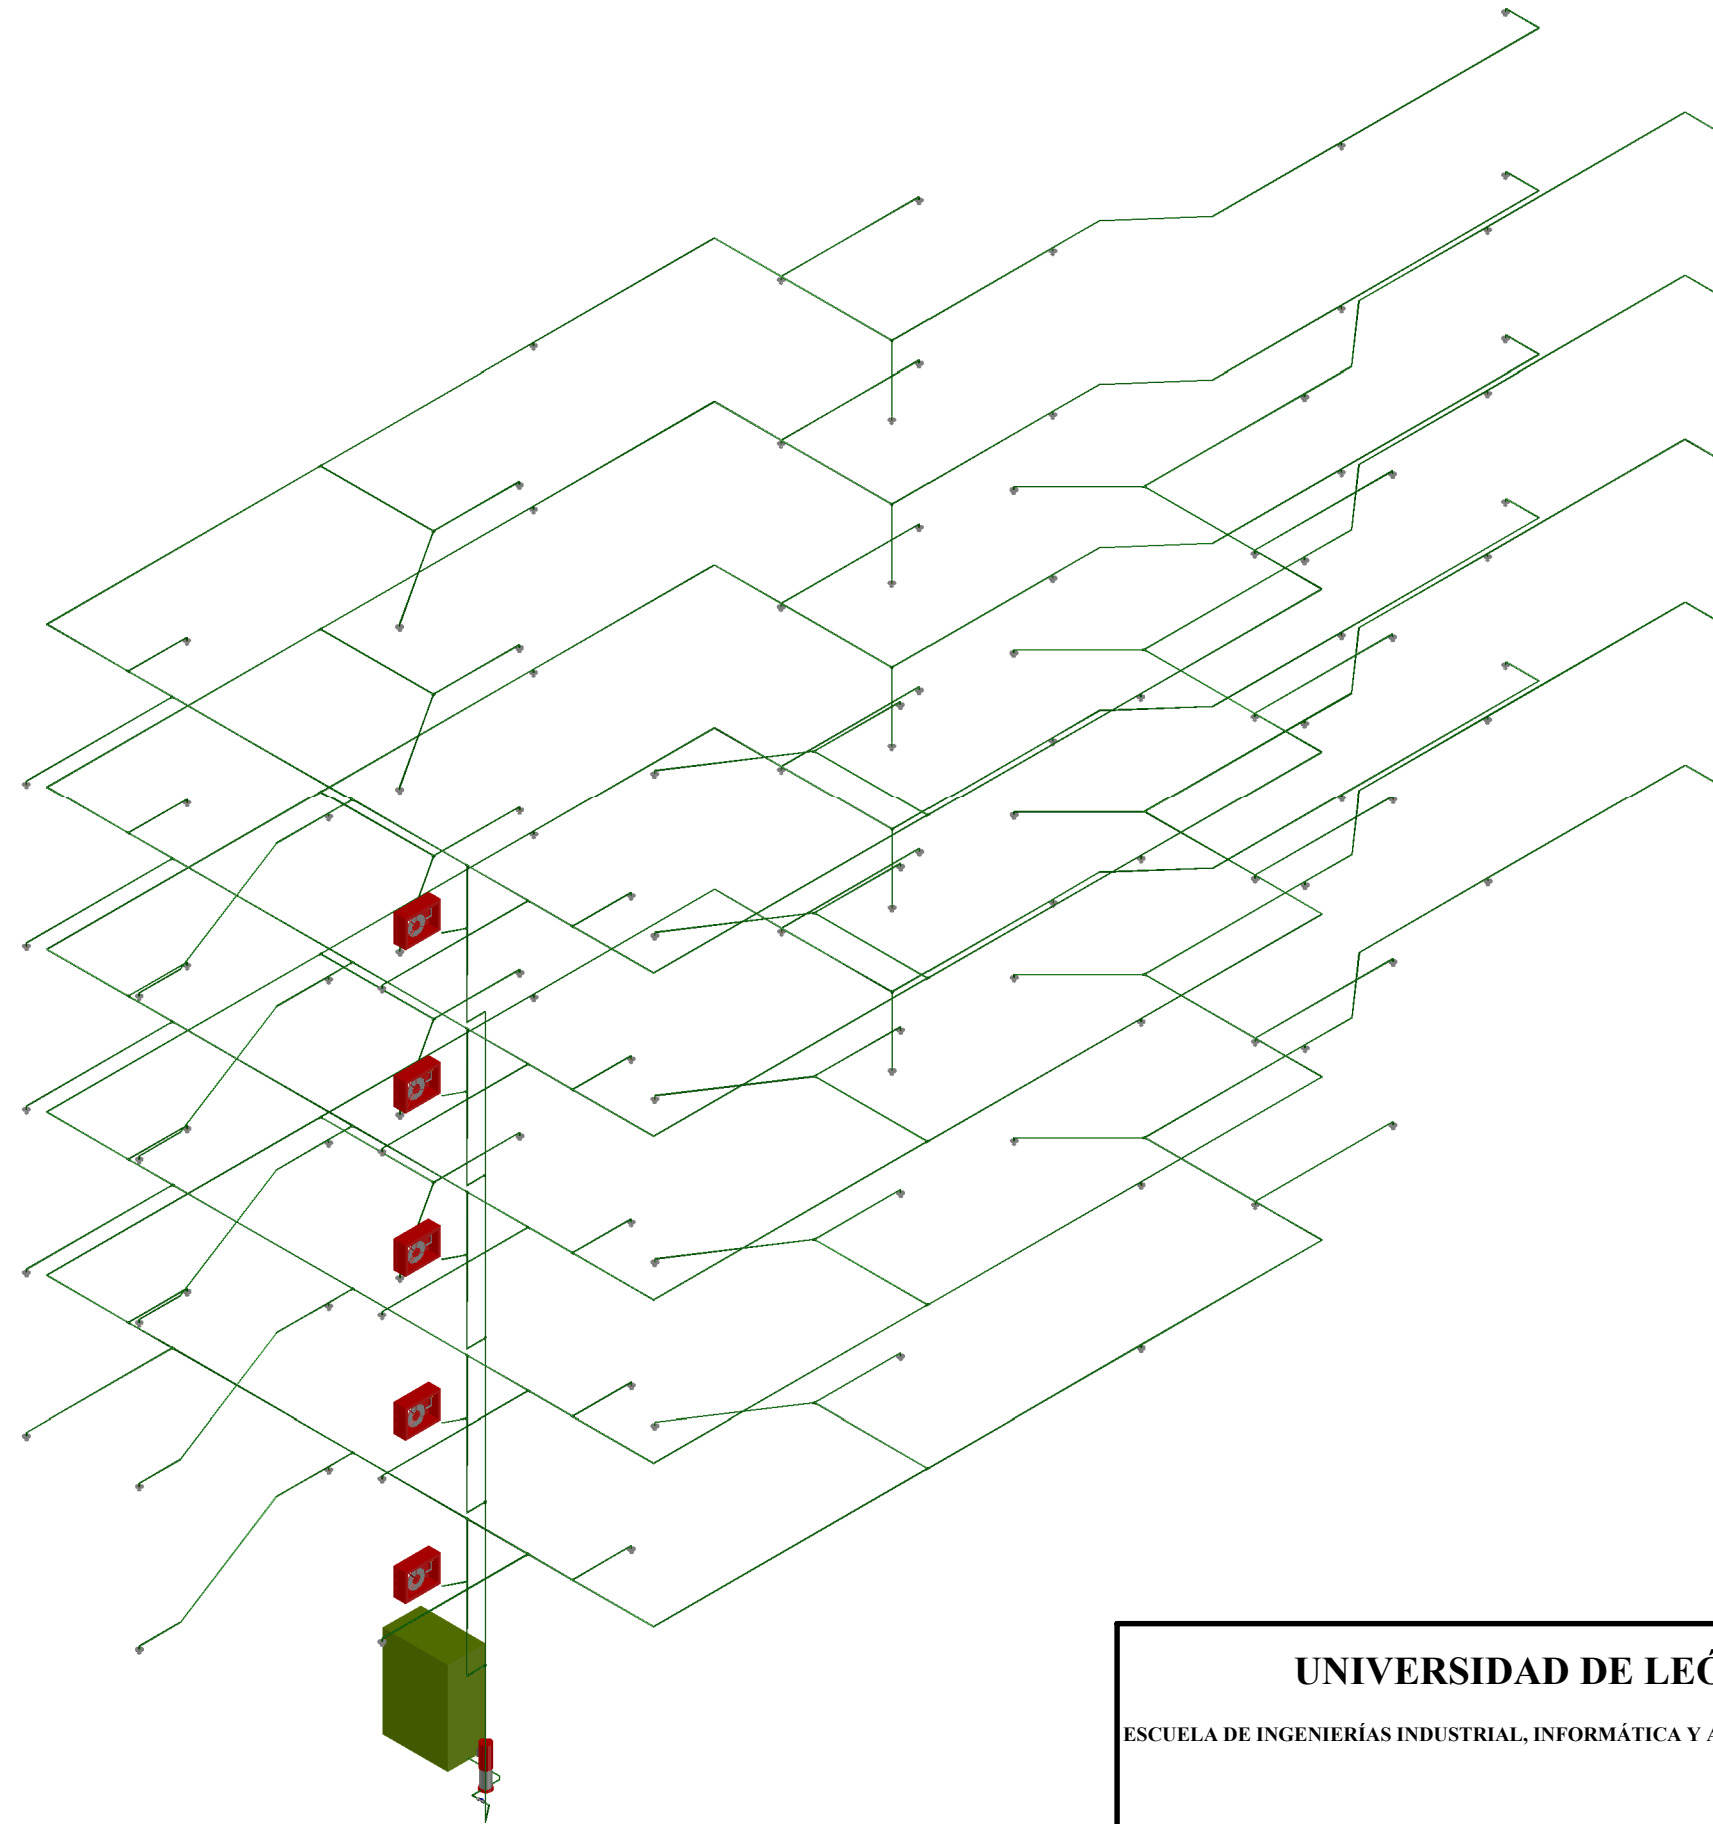

UNIVERSIDAD DE LEÓN ESCUELA DE INGENIERÍAS INDUSTRIAL, INFORMÁTICA Y AEROSPAIAL		PROYECTO: PRÁCTICA DE PROTECCIÓN CONTRA INCENDIOS		
PLANO: PLANO ISOMÉTRICO DE LA INSTALACIÓN PCI		ESCALA: 1:250	FECHA: 06/2026	Nº PLANO: 4
LOS ALUMNOS: Alberto España Carrete Rubén Modino López		PRÁCTICA INSTALACIONES II		