


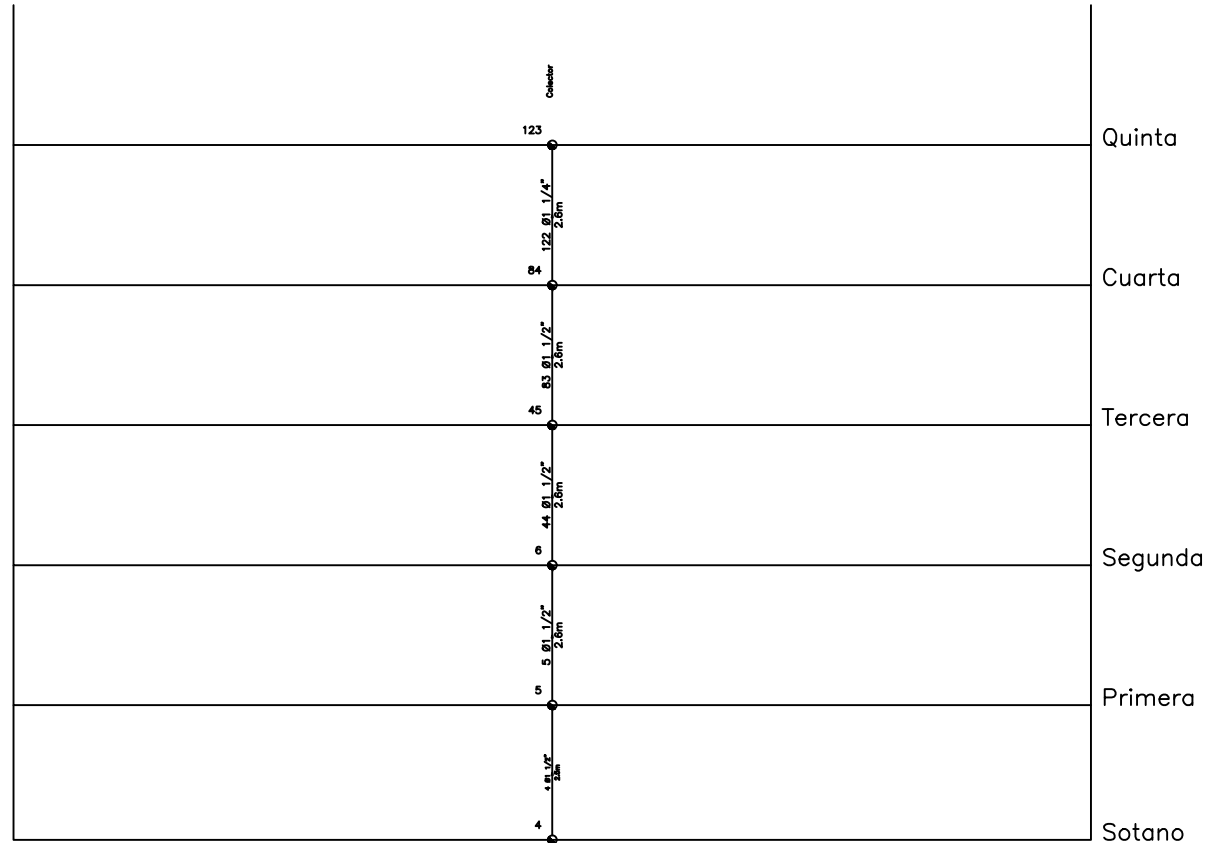

UNIVERSIDAD DE LEÓN
ESCUELA DE INGENIERÍAS INDUSTRIAL, INFORMÁTICA Y AEROESPACIAL

PLANO: INSTALACIÓN COMÚN (MONTANTES)

LOS ALUMNOS:

Alberto España Carrete
Rubén Modino López

PROYECTO:

PRÁCTICA DE PROTECCIÓN
CONTRA INCENDIOS

ESCALA:
1:150

FECHA:
06/2026

PRÁCTICA INSTALACIONES II

Nº PLANO:

3