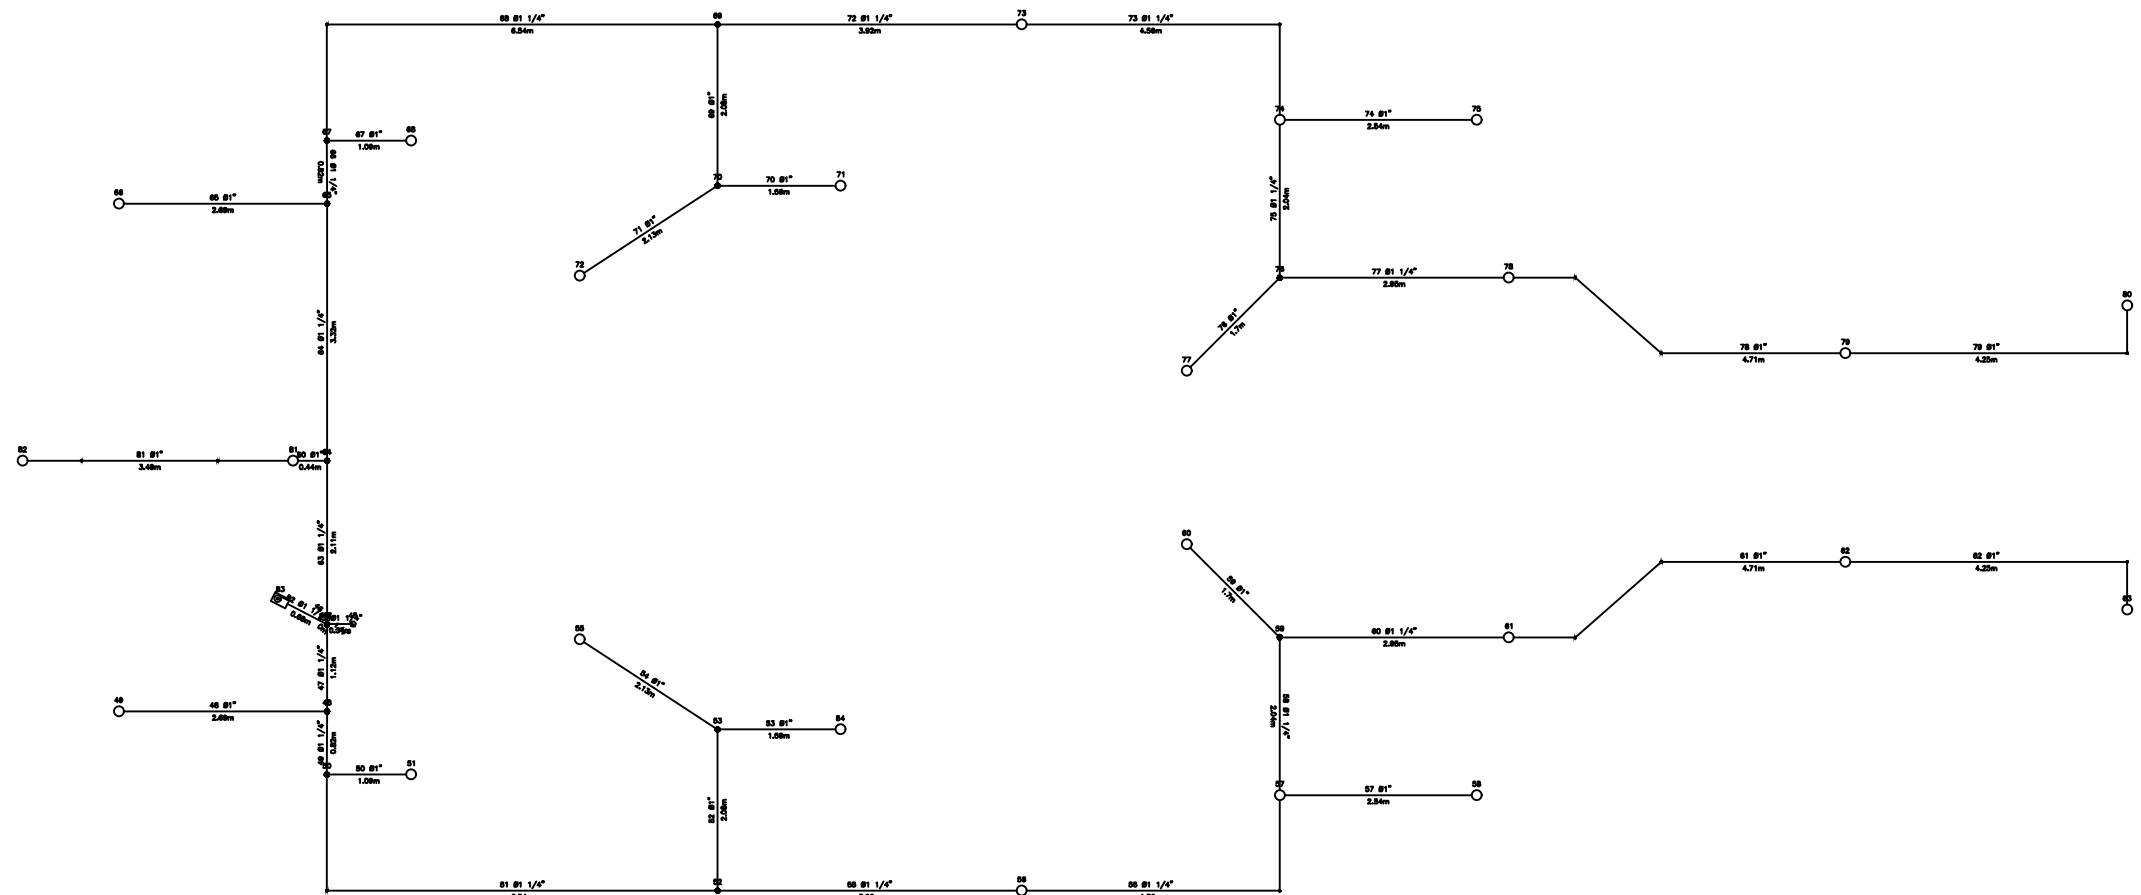


UNIVERSIDAD DE LEÓN ESCUELA DE INGENIERÍAS INDUSTRIAL, INFORMÁTICA Y AEROSPAECIAL		PROYECTO: PRÁCTICA DE PROTECCIÓN CONTRA INCENDIOS	
PLANO: ESQUEMA DE PLANTAS SÓTANO Y 1ª		ESCALA: 1:25 1:100	FECHA: 06/2026
LOS ALUMNOS: Alberto España Carrete Rubén Modino López		Nº PLANO: 2	
		PRÁCTICA INSTALACIONES II	