


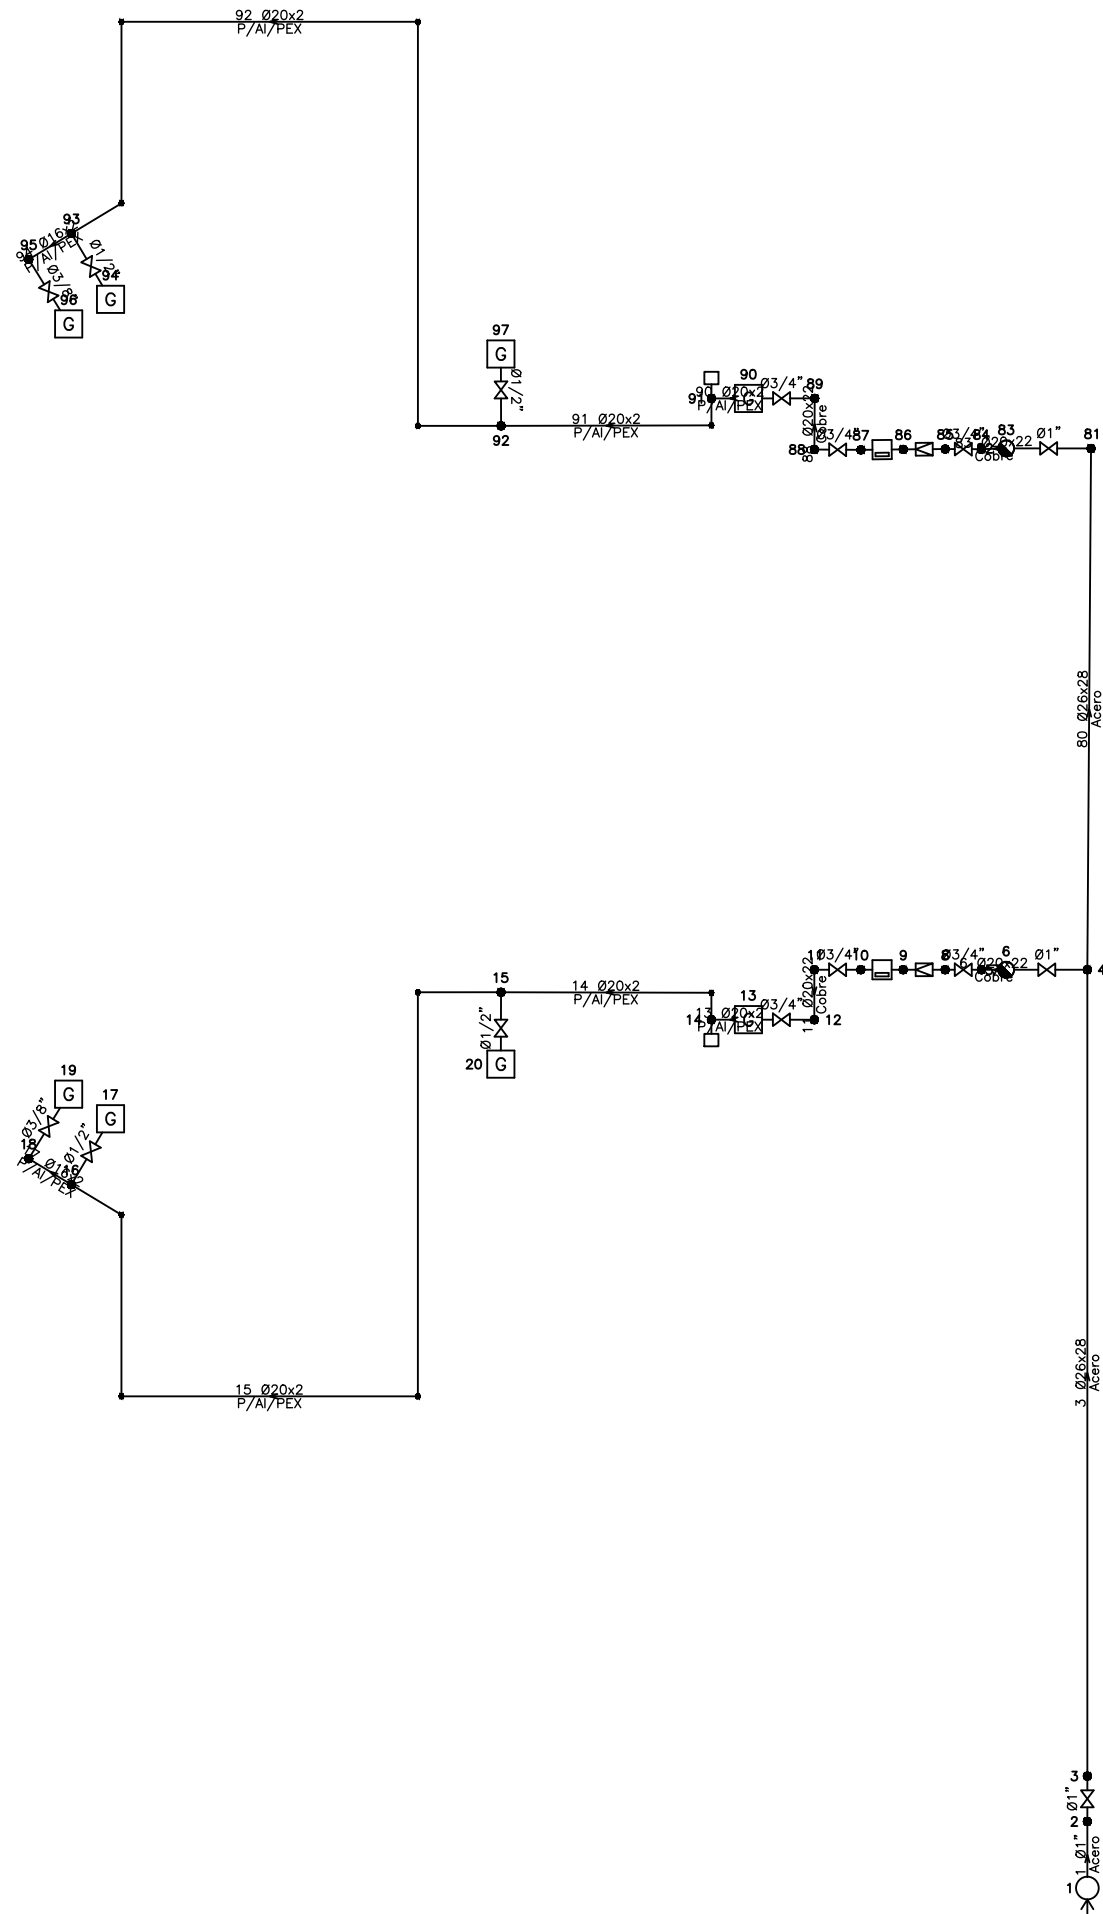

ACCESORIOS	
	Nombre
	Conexión entre plantas
	Conexión a red
	Derivación o conexión ramas diferentes
	Llave de paso
	Aparato de utilización
	Codo
	Toma de presión
	Regulador de presión
	Contador gas

UNIVERSIDAD DE LEÓN ESCUELA DE INGENIERÍAS INDUSTRIAL, INFORMÁTICA Y AEROESPACIAL	PROYECTO:		
	PRÁCTICA DE GAS NATURAL		
	PLANO:	ESCALA:	FECHA:
ESQUEMA ACOMETIDA-INSTALACIÓN INDIVIDUAL		1/50	05/2026
LOS ALUMNOS:		PRÁCTICA INSTALACIONES II	
Alberto España Carrete Carlos Fernández Palanca Ruben Modino López Juan Diego Niño González		2	