


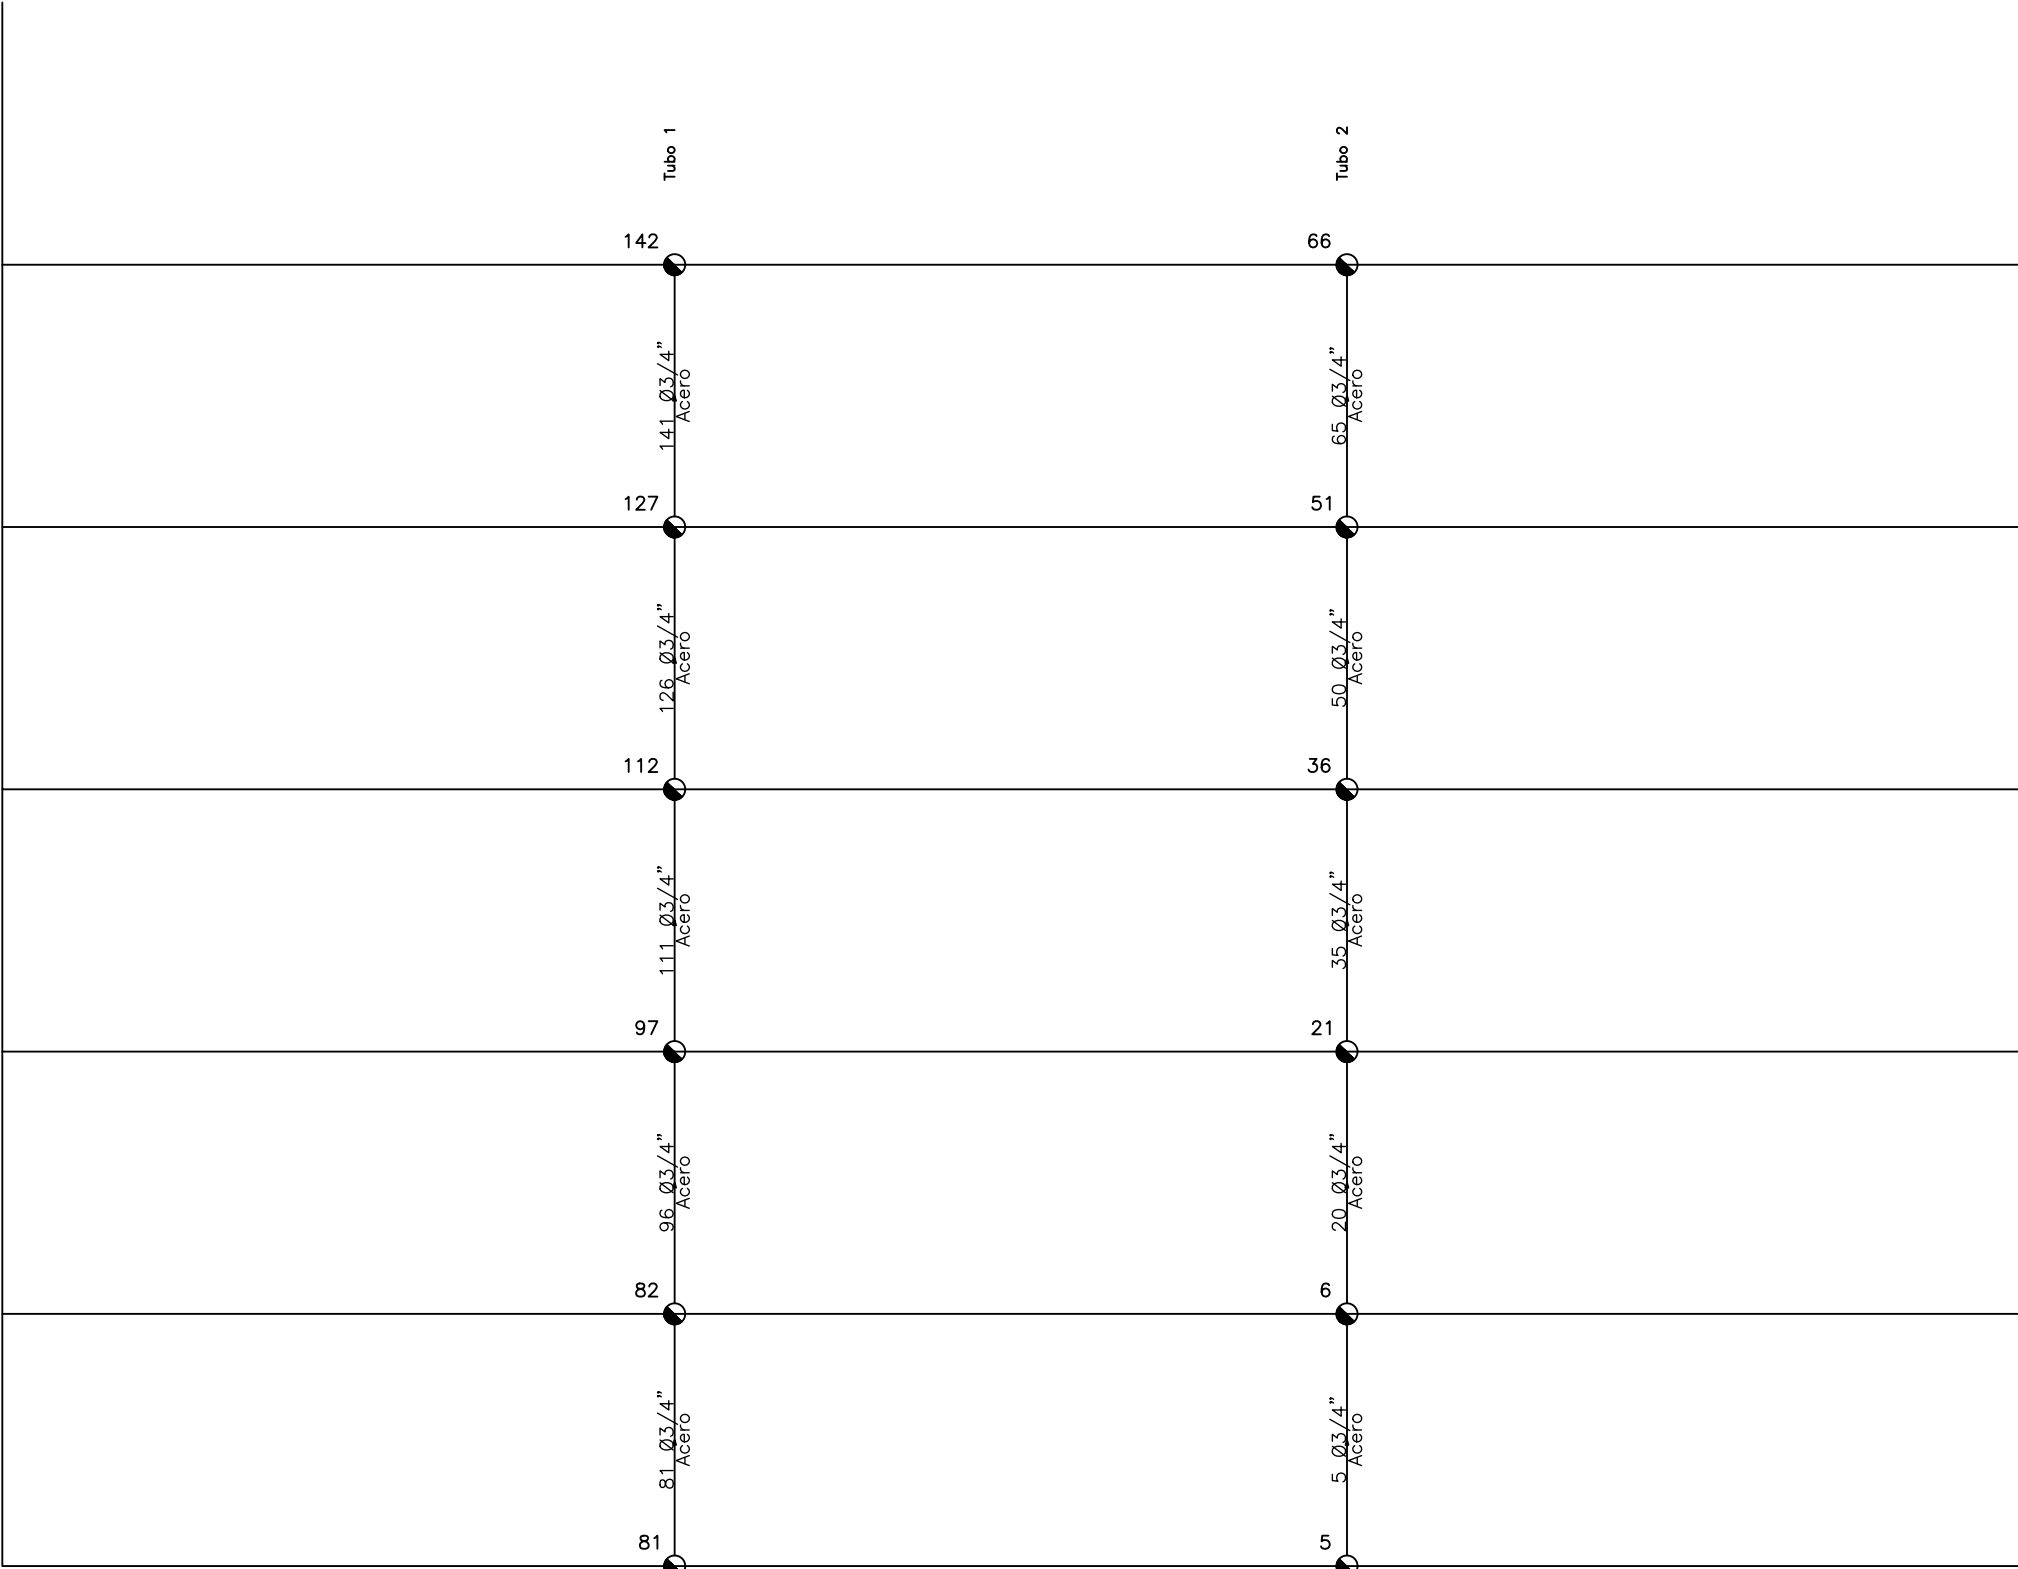

Quinta

Cuarta

Tercera

Segunda

Primera

Baja

UNIVERSIDAD DE LEÓN

ESCUELA DE INGENIERÍAS INDUSTRIAL, INFORMÁTICA Y AEROESPACIAL

PLANO:

INSTALACIÓN COMÚN (MONTANTES)

LOS ALUMNOS:

Alberto España Carrete
Carlos Fernández Palanca
Ruben Modino López
Juan Diego Niño González

PROYECTO:

PRÁCTICA DE GAS NATURAL

ESCALA:

1/75

FECHA:

05/2026

Nº PLANO:

3

PRÁCTICA INSTALACIONES II